

650.292.0752

Architect/Engineer

VEEV

Project

Plan Number: **P1016**

# SFH2X

Designer of Record Stamp



PLAN CHECK AUTHORITY (DAA)

STATE ☒ LOCAL

INSPECTION AUTHORITY (QAA)

FACTORY BUILT  
HOUSING WORK  
DRAWN IN BLACK

| STATE INSPECTION | LOCAL INSPECTION |
|------------------|------------------|
|------------------|------------------|

STATE  
INSPECTIO

## LOCAL SPECTION

---


---

Approved: State of CA  
 Certified Design Approval Agency - ICC NTA, LLC. 920268  
 Approved: Factory Built Housing

ICC NTA, LLC. Plan Approval: VEFV053025-60

Approval Date: 9/3/2025

Expiration Date: 7/11/2028

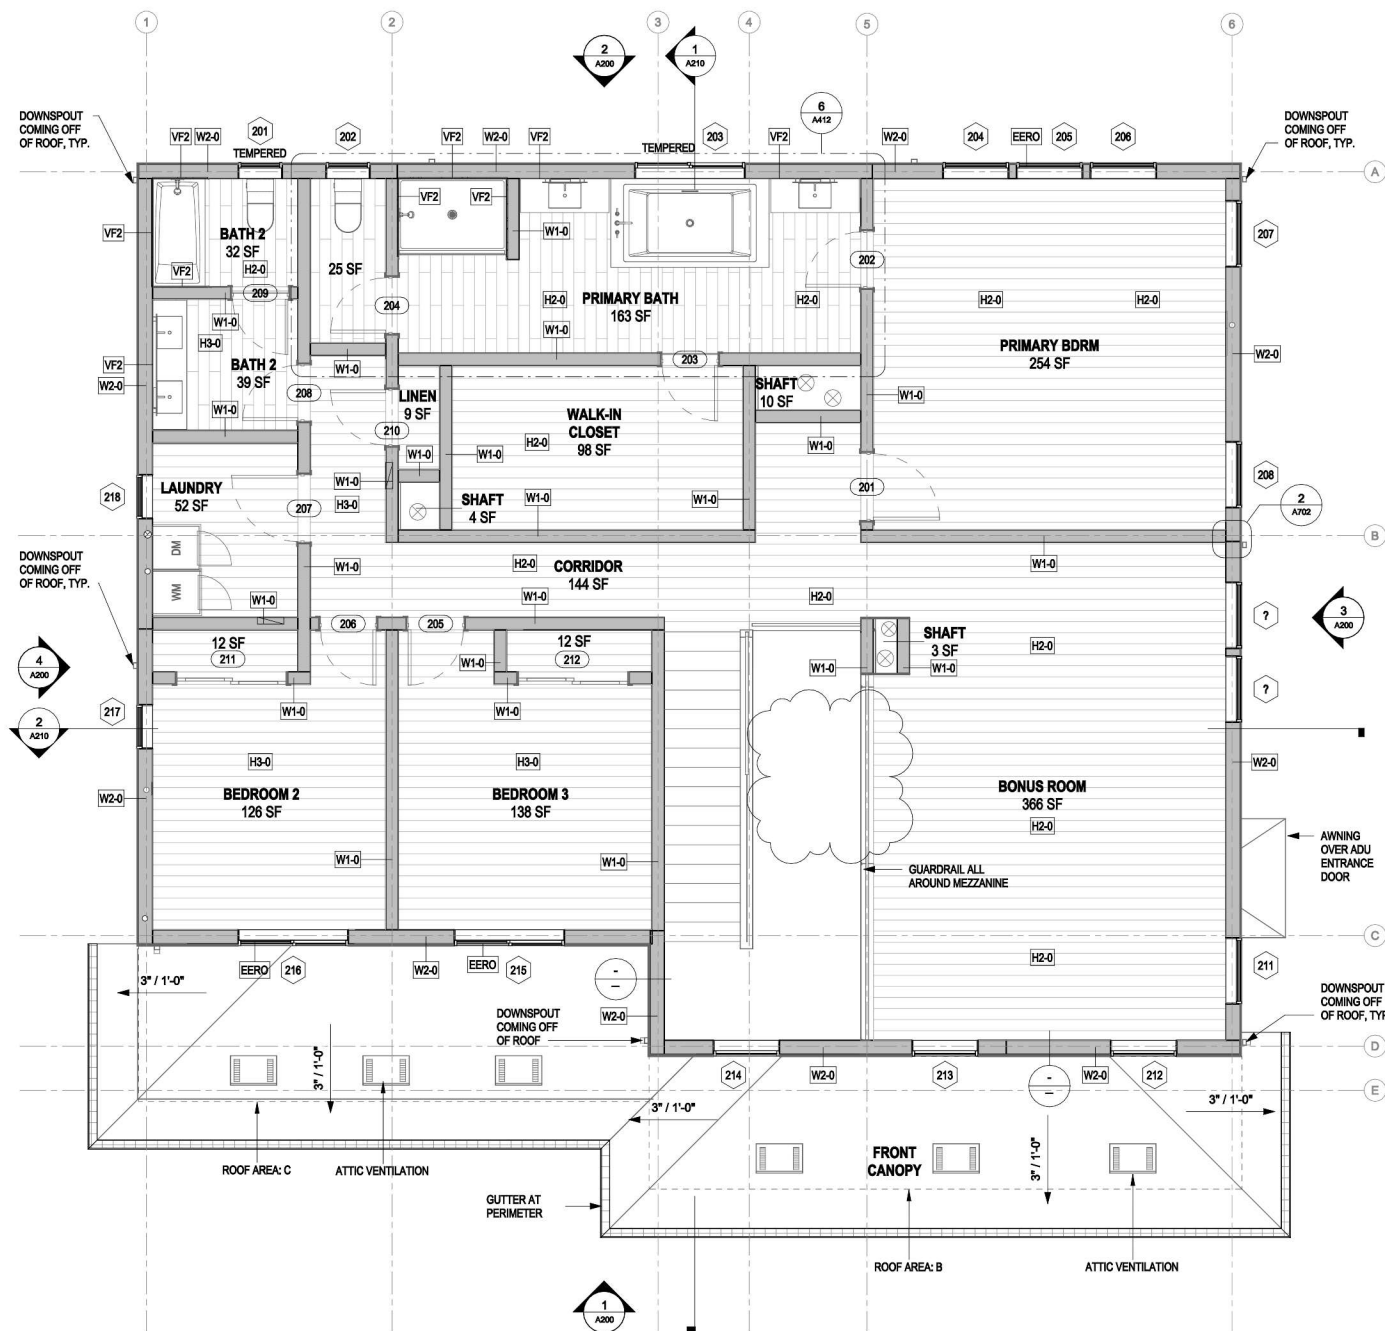

1 FLOOR PLAN - SECOND FLOOR  
1/4" = 1'-0"

## ATTIC VENTILATION METHOD

| ATTIC | ATTIC SQ. FT. | APPLIED RULES OR EXCEPTIONS | SQUARE INCHES NFVA* REQUIRED | HIGH/LOW VENTING PROVIDED (U.N.O.)                | SQUARE INCHES NFVA* PROVIDED |
|-------|---------------|-----------------------------|------------------------------|---------------------------------------------------|------------------------------|
| A     | 1871          | 1/300                       | 898                          | 7 HIGH AND 7 LOW VENTS AT 72 SQ. IN. N.F.V.A EACH | 1008                         |
| B     | 159           | 1/150                       | 152                          | 3 VENTS AT 72 SQ. IN. N.F.V.A EACH                | 216                          |
| C     | 162           | 1/150                       | 156                          | 3 VENTS AT 72 SQ. IN. N.F.V.A EACH                | 216                          |

ALL REQUIRED ATTIC VENTILATION SHALL COMPLY WITH THE CALIFORNIA RESIDENTIAL CODE SECTION R 806 - ROOF VENTILATION.  
DO NOT INSTALL VENTS BELOW AREAS OF CONCENTRATED WATER RUNOFF . PLACEMENT ASSUMES GUTTERS ARE INSTALLED IN ALL APPLICABLE AREAS.  
INSTALLATION SHALL FOLLOW MANUFACTURER SPECIFICATIONS.  
VENTS IN WILD URBAN INTERFACE (WUI) APPLICATION SHALL BE COMPLIANT WITH R 337.6.  
CRICKETS SHALL HAVE A MIN. SLOPE OF 1/4" TO 1'.

## GENERAL NOTES

1. GRIDLINES ARE TO CENTERLINE OF STUD U.O.N.
2. ALL CEILINGS ARE SITE INSTALLED
3. SEE SHEET A700 FOR TYPICAL HORIZONTAL ASSEMBLIES
4. SEE SHEET A701 FOR TYPICAL VERTICAL ASSEMBLIES
5. ALL STEEL SHEET METAL FLASHING, FURRING, FRAMING, ETC. LOCATED EXTERIOR TO WEATHER BARRIER TO BE GALVANIZED G60 OR GREATER.
6. SLOPE GUTTERS MIN 1/16" PER FOOT
7. EXTERIOR FINISH CLADDING VARIES PER PROJECT. SEE A700 AND A701 FOR FINISH CLADDING OPTIONS, AND LOCAL DRAWINGS FOR SPECIFIC CLADDING TYPE LAYOUT.

## ASSEMBLY ID LEGEND

1. 2. 3.
- 
- 1. BUILDING ELEMENT**  
H = BASE HORIZONTAL ASSEMBLY  
W = WALL ASSEMBLY
- 2. UNIQUE ID**
- 3. FIRE RESISTANCE RATING**  
0 = NON-RATED  
5 = 30 MINUTES  
1 = 1-HOUR  
2 = 2-HOUR

## LEGEND

- |                                                                                     |   |
|-------------------------------------------------------------------------------------|---|
|  | DOOR TAG, SEE SHEET A600                                                                                           |
|  | WINDOW TAG, SEE SHEET A600                                                                                         |
|  | NEW UNRATED CONSTRUCTION                                                                                           |
|  | BUILDING FIRE ALARM SYSTEM LOW FREQUENCY HORN, PROVIDED AND INSTALLED BY FIRE ALARM SYSTEM DESIGN-BUILD CONTRACTOR |
|  | ATTIC VENTILATION                                                                                                  |

## FLOOR FINISH

SEE A700 FOR ASSEMBLY DEFINITIONS

- 

## WALL FINISH

SEE A701 FOR ASSEMBLY DEFINITIONS

- VF1 - TYPICAL FINISH UON (PAINTED DRYWALL)

- VF2 - THINSET TILE (AROUND BATHTUBS, SHOWERS, KITCHEN & BATHROOM, BACKSPASH\*).**

- \*BACKSPLASH:  
IN BATHROOMS - 4" ABOVE VANITIES.  
IN KITCHEN - BETWEEN COUNTERTOP AND UPPER CABINETS  
THROUGHOUT

[illegible]

|          |           |                              |
|----------|-----------|------------------------------|
| Drawn    | <b>LO</b> | Scale<br><b>As Indicated</b> |
| Checked  | <b>NG</b> |                              |
| Approved | <b>MH</b> |                              |

Sheet Name:

FLOOR PLAN - SECOND FLOOR

Sheet Number

A102

Project  
**P1016**

Issue/Review

Autodesk Docs://P1016 - SFH2X/P1016-NTA.m

8/29/2025 11:48:40